



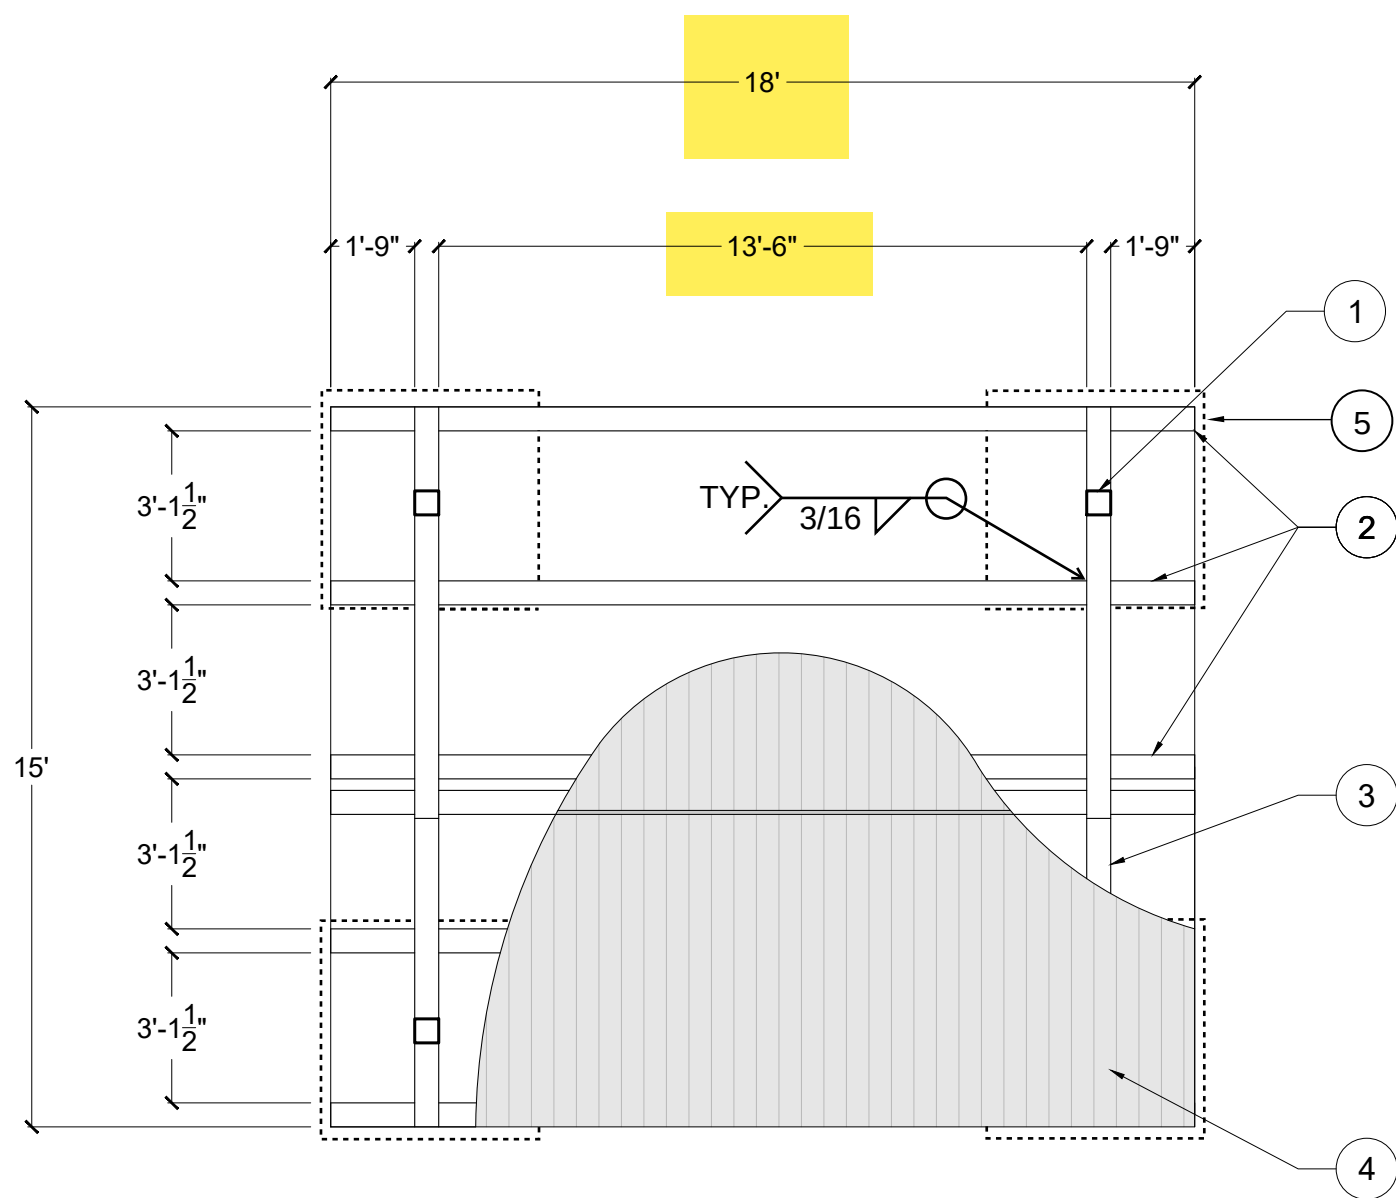



1 TOP ELEVATION
SCALE 1/4" = 1'

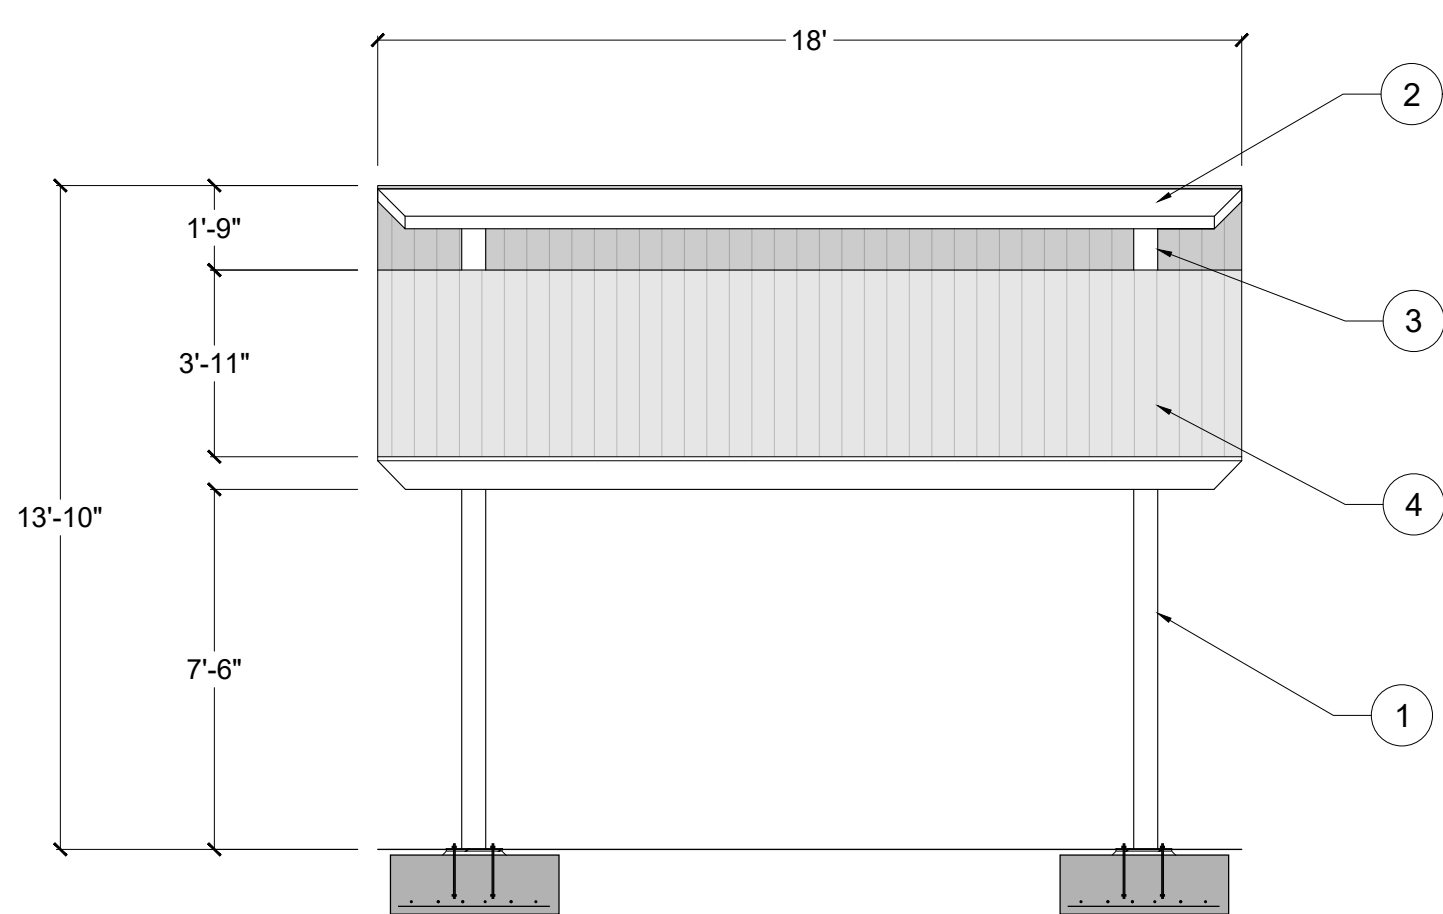

2 SIDE ELEVATION
SCALE 1/4" = 1'


MATERIAL SPECIFICATIONS:

1. HSS6X6X3/16 COLUMN
2. HSS8X6X3/16 BEAM
3. HSS8X6X3/16 RAFTER BEAM
4. WESTERN LOCK STANDING SEAM ROOF, 16" WIDE X 24 GAUGE, NO UNDERLAYMENT.
5. TYP. 4'-6" SQ. FOOTING PER DETAIL A.

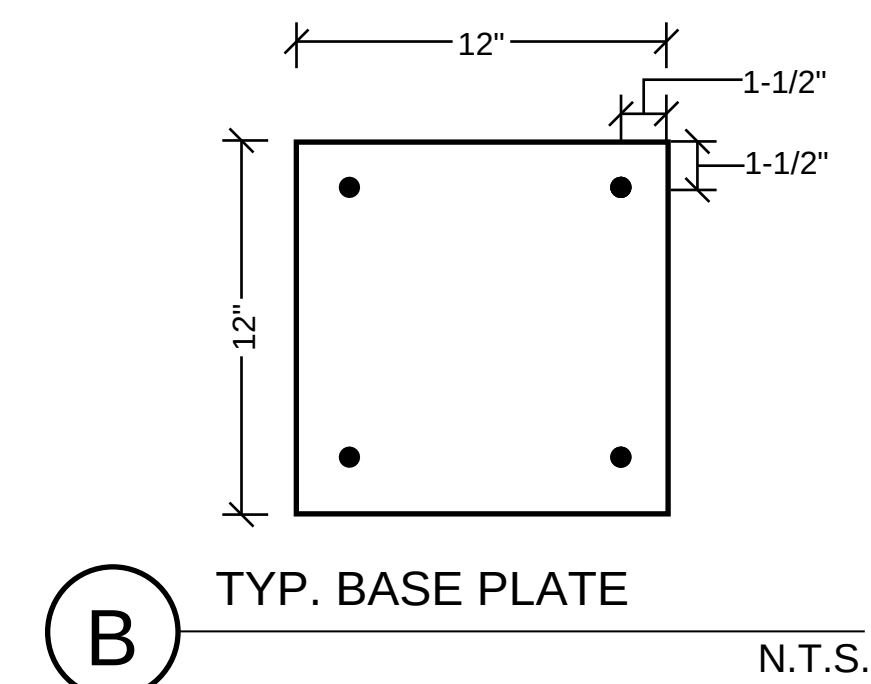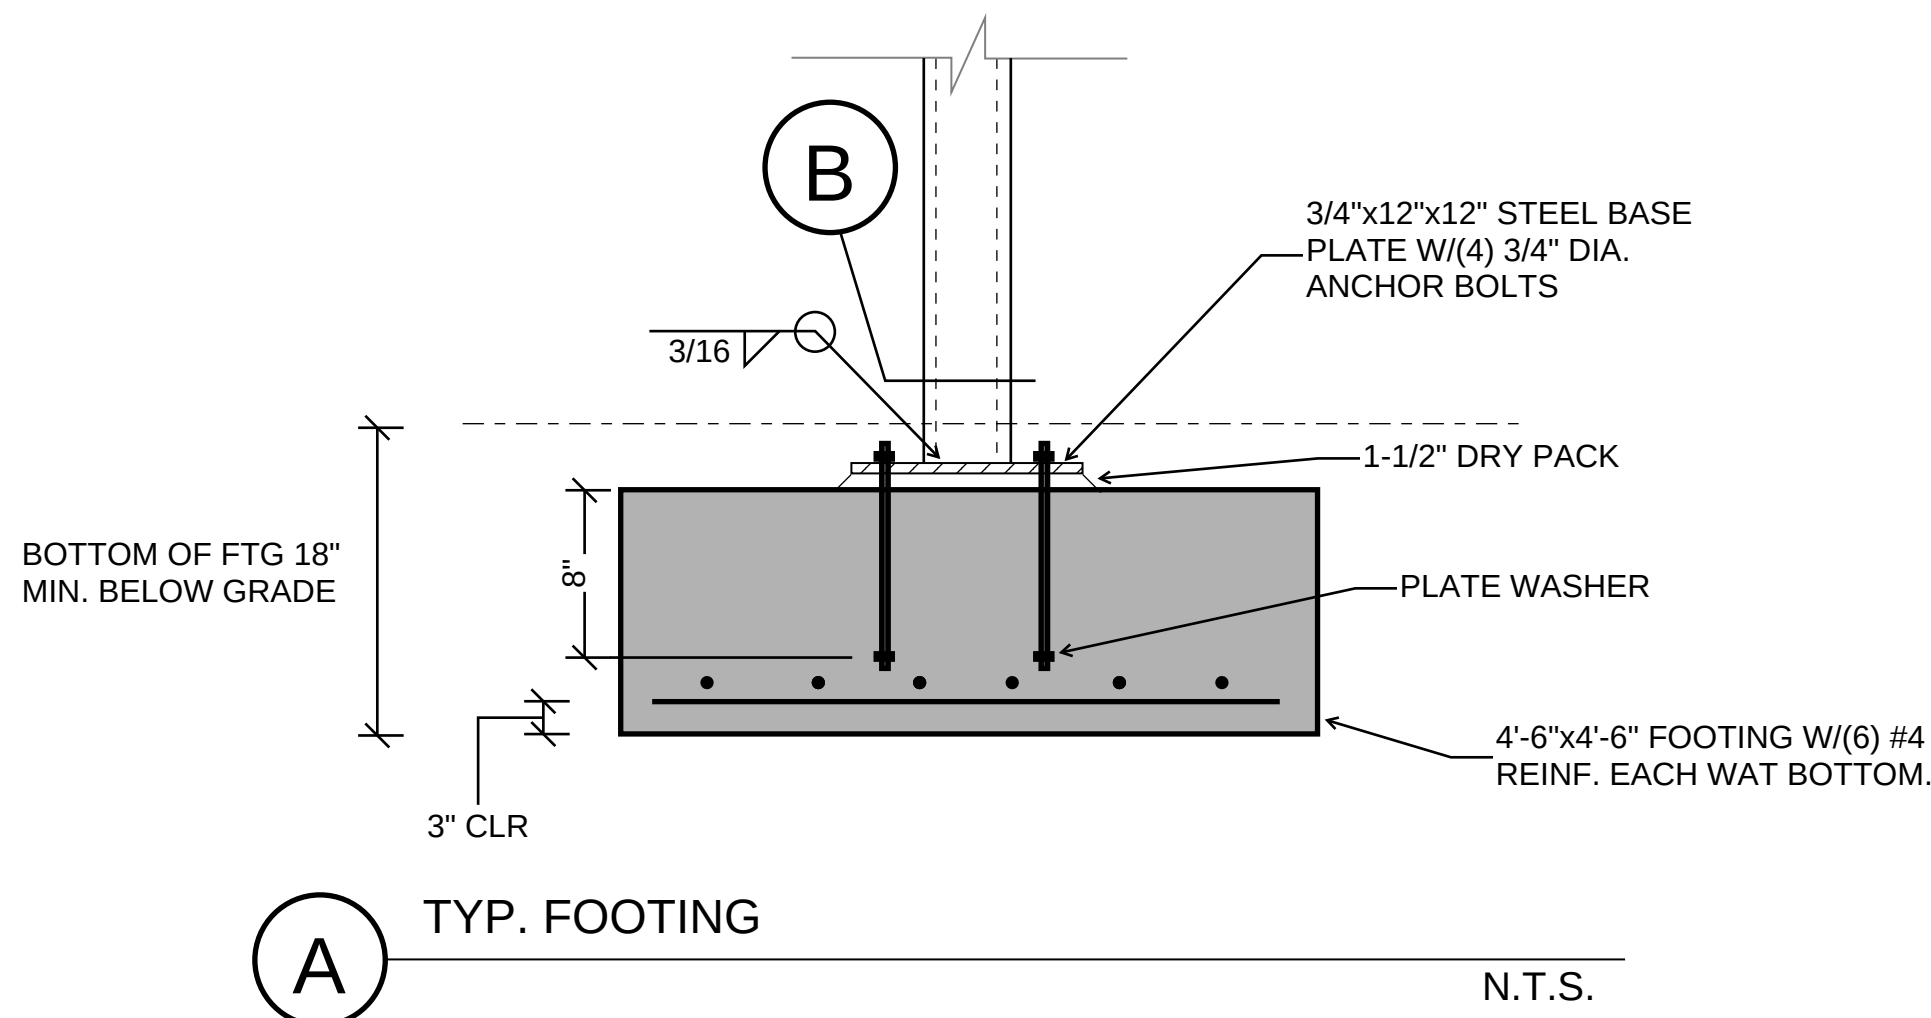

Seal Applies Only to "SADDLE BACK VILLAGE - RAMADAS" Structural Content ALL DIMENSIONS AND MATERIAL SHALL BE APPROVED BY THE OWNER OR LANDSCAPE ARCHITECT PRIOR TO FABRICATION

(2)

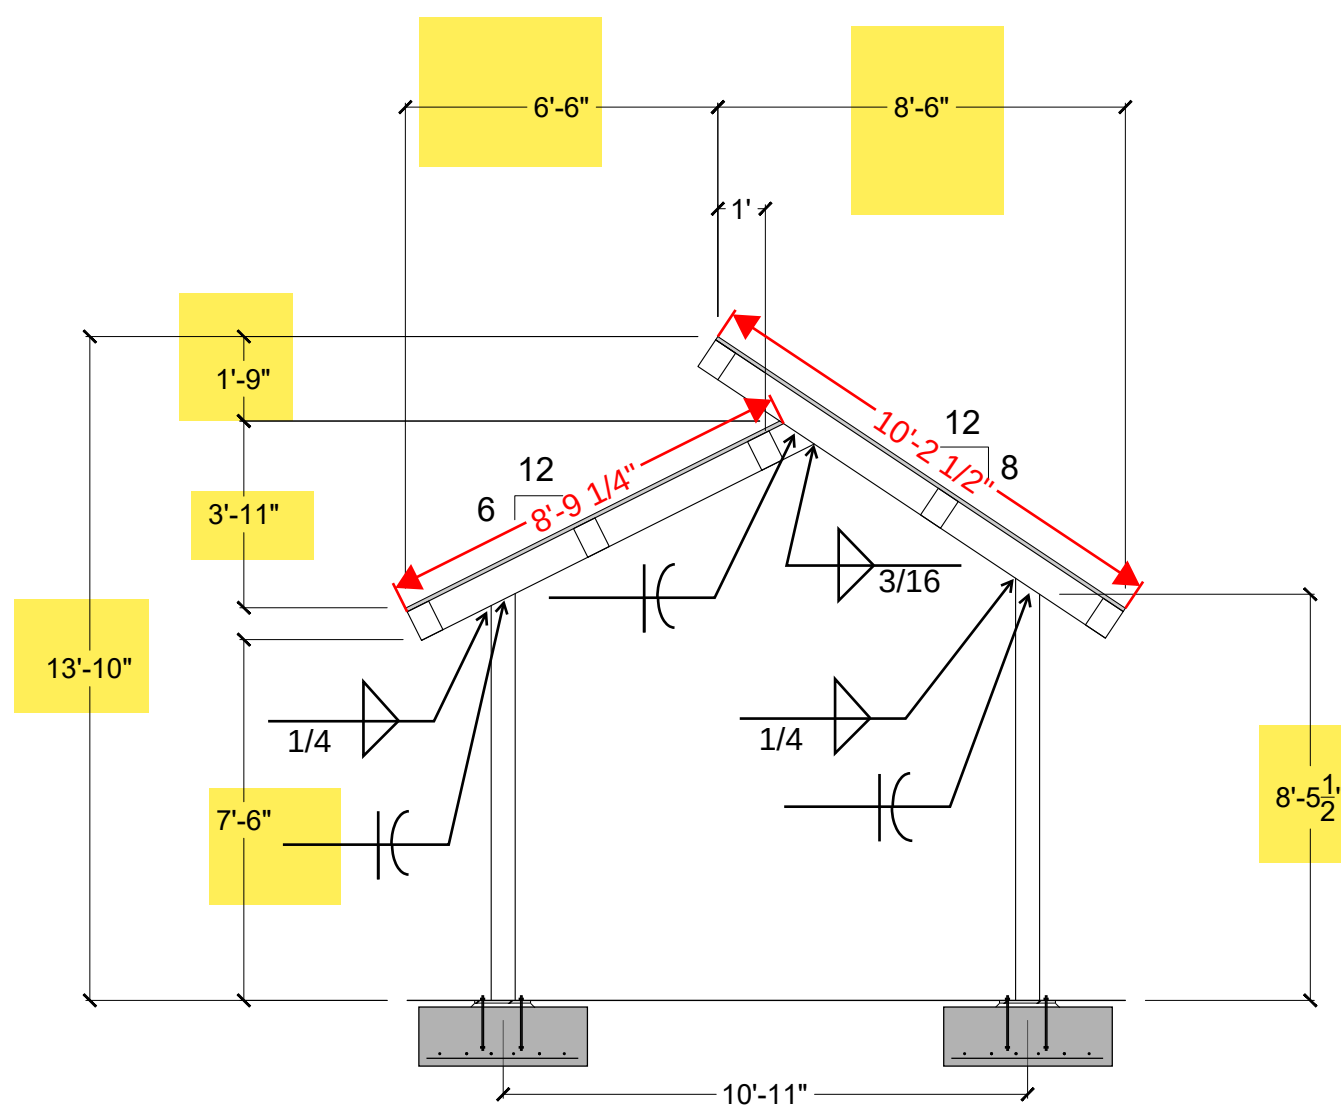

3 FRONT ELEVATION
SCALE 1/4" = 1'

REVISIONS		
NO.	DESCRIPTION	DATE
1		
2		
3		
4		
5		
6		
7		

PROJECT:
SADDLEBACK VILLAGE
LONE MOUNTAIN & VISTANCIA BLVD. PEORIA, AZ 85383
15' X 18' RAMADA

DRAWN	PA
CHECKED	WA
DATE	08/15/2025
SCALE	AS INDICATED
JOB	SADDLEBACK
SHEET	1.1